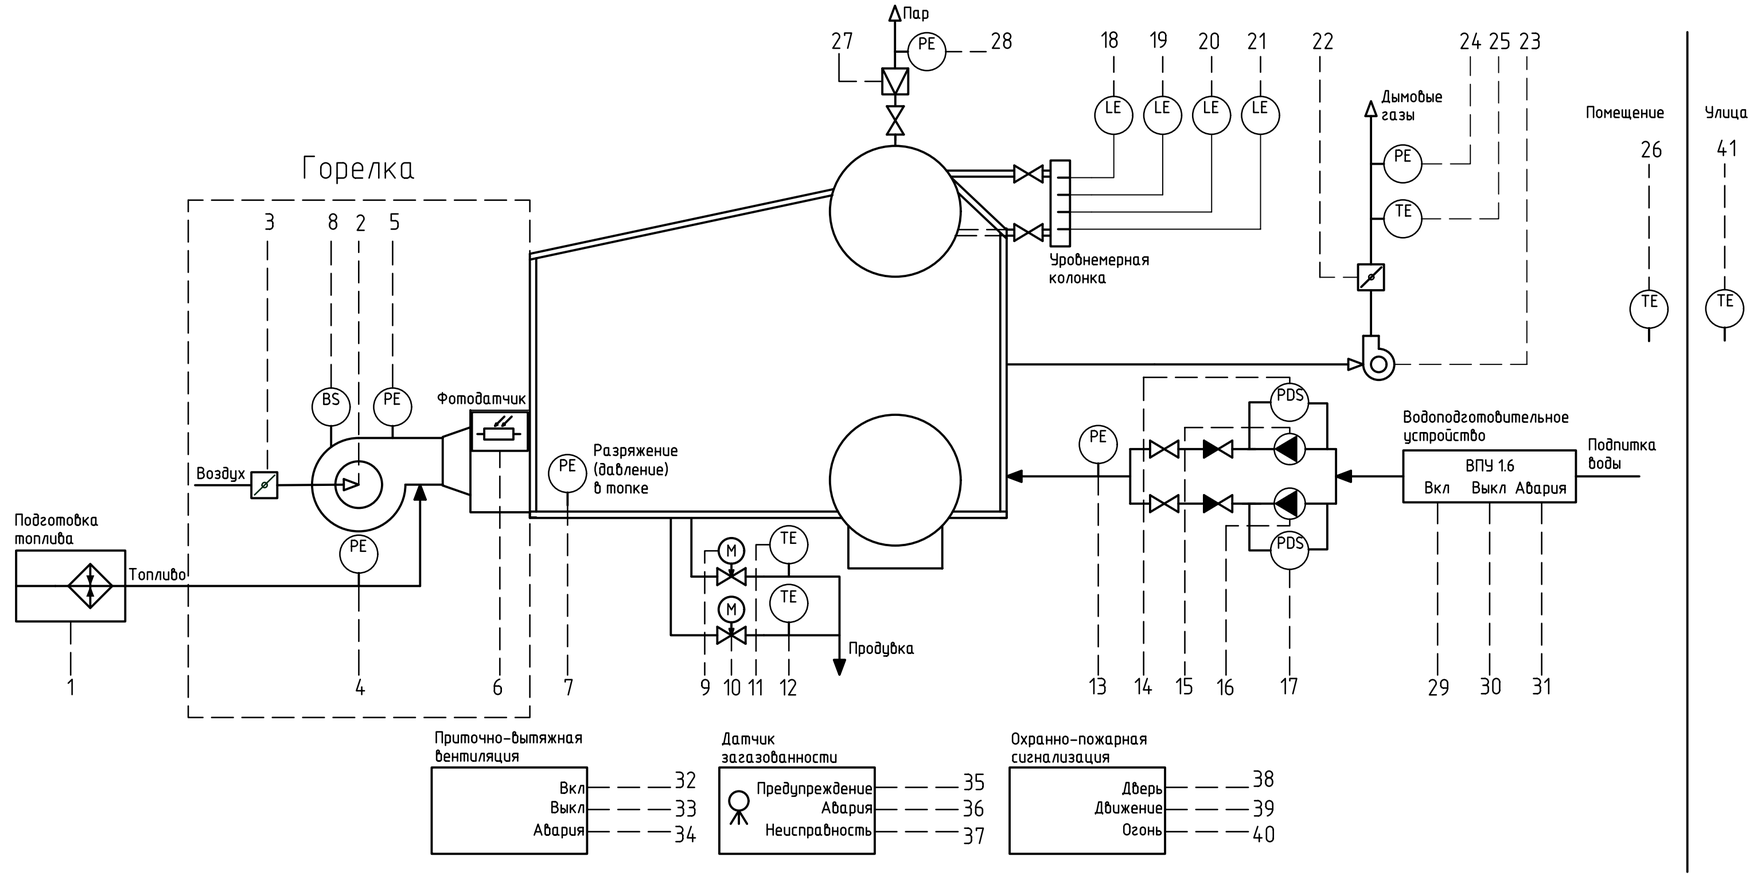


Автоматика котельной			1	2	3	4	5	6	7	8	9	10	11	12	13	14	15	16	17	18	19	20	21	22	23	24	25	26	27	28	29	30	31	32	33	34	35	36	37	38	39	40	41
			подогрев топлива	вентилятор	воздушная заслонка	датчик давления топлива	датчик давления воздуха	датчик наличия пламени	датчик давления в топке	реле давления воздуха	клапан нижней продувки 1	клапан нижней продувки 2	датчик неисправности кл. прод. 1	датчик неисправности кл. прод. 2	датчик давления воды	диф. реле резервного насоса	основной насос подпитки	резервный насос подпитки	диф. реле резервного насоса	датчик ВАУ	датчик ВРУ	датчик НРУ	датчик НАУ	заслонка на дымососе	вентилятор дымососа	датчик давления дым. газов	температура ды. газов	температура воздуха в помещении	расходомер пара	давление пара	включить ВПУ	выключить ВПУ	авария ВПУ	включить вентиляцию	выключить вентиляцию	авария вентиляции	датчик загазованности предупреждение	датчик загазованности авария	датчик загазованности неисправность	ОПС дверь открыта	ОПС движение	ОПС огонь в помещении	температура на улице
Шкаф автоматики	аналоговый ввод												•	•														•	•														•
	аналоговый вывод																			•	•	•	•																					
	дискретный ввод															•	•			•	•	•	•											•			•	•	•				•	
	дискретный вывод	•									•	•						•	•											•	•	•		•	•					•	•	•	
горелочное устройство				•	•	•	•	•	•	•					•									•	•	•	•	•	•														